


CIQ GATEWAY SITE ANALYSIS

Shared Ground & Urban Quarter in Sheffield


Registration No. 250206144
Word Count: 1082 words
Submission Date: 26/01/2026




STRATEGIC CONTEXT

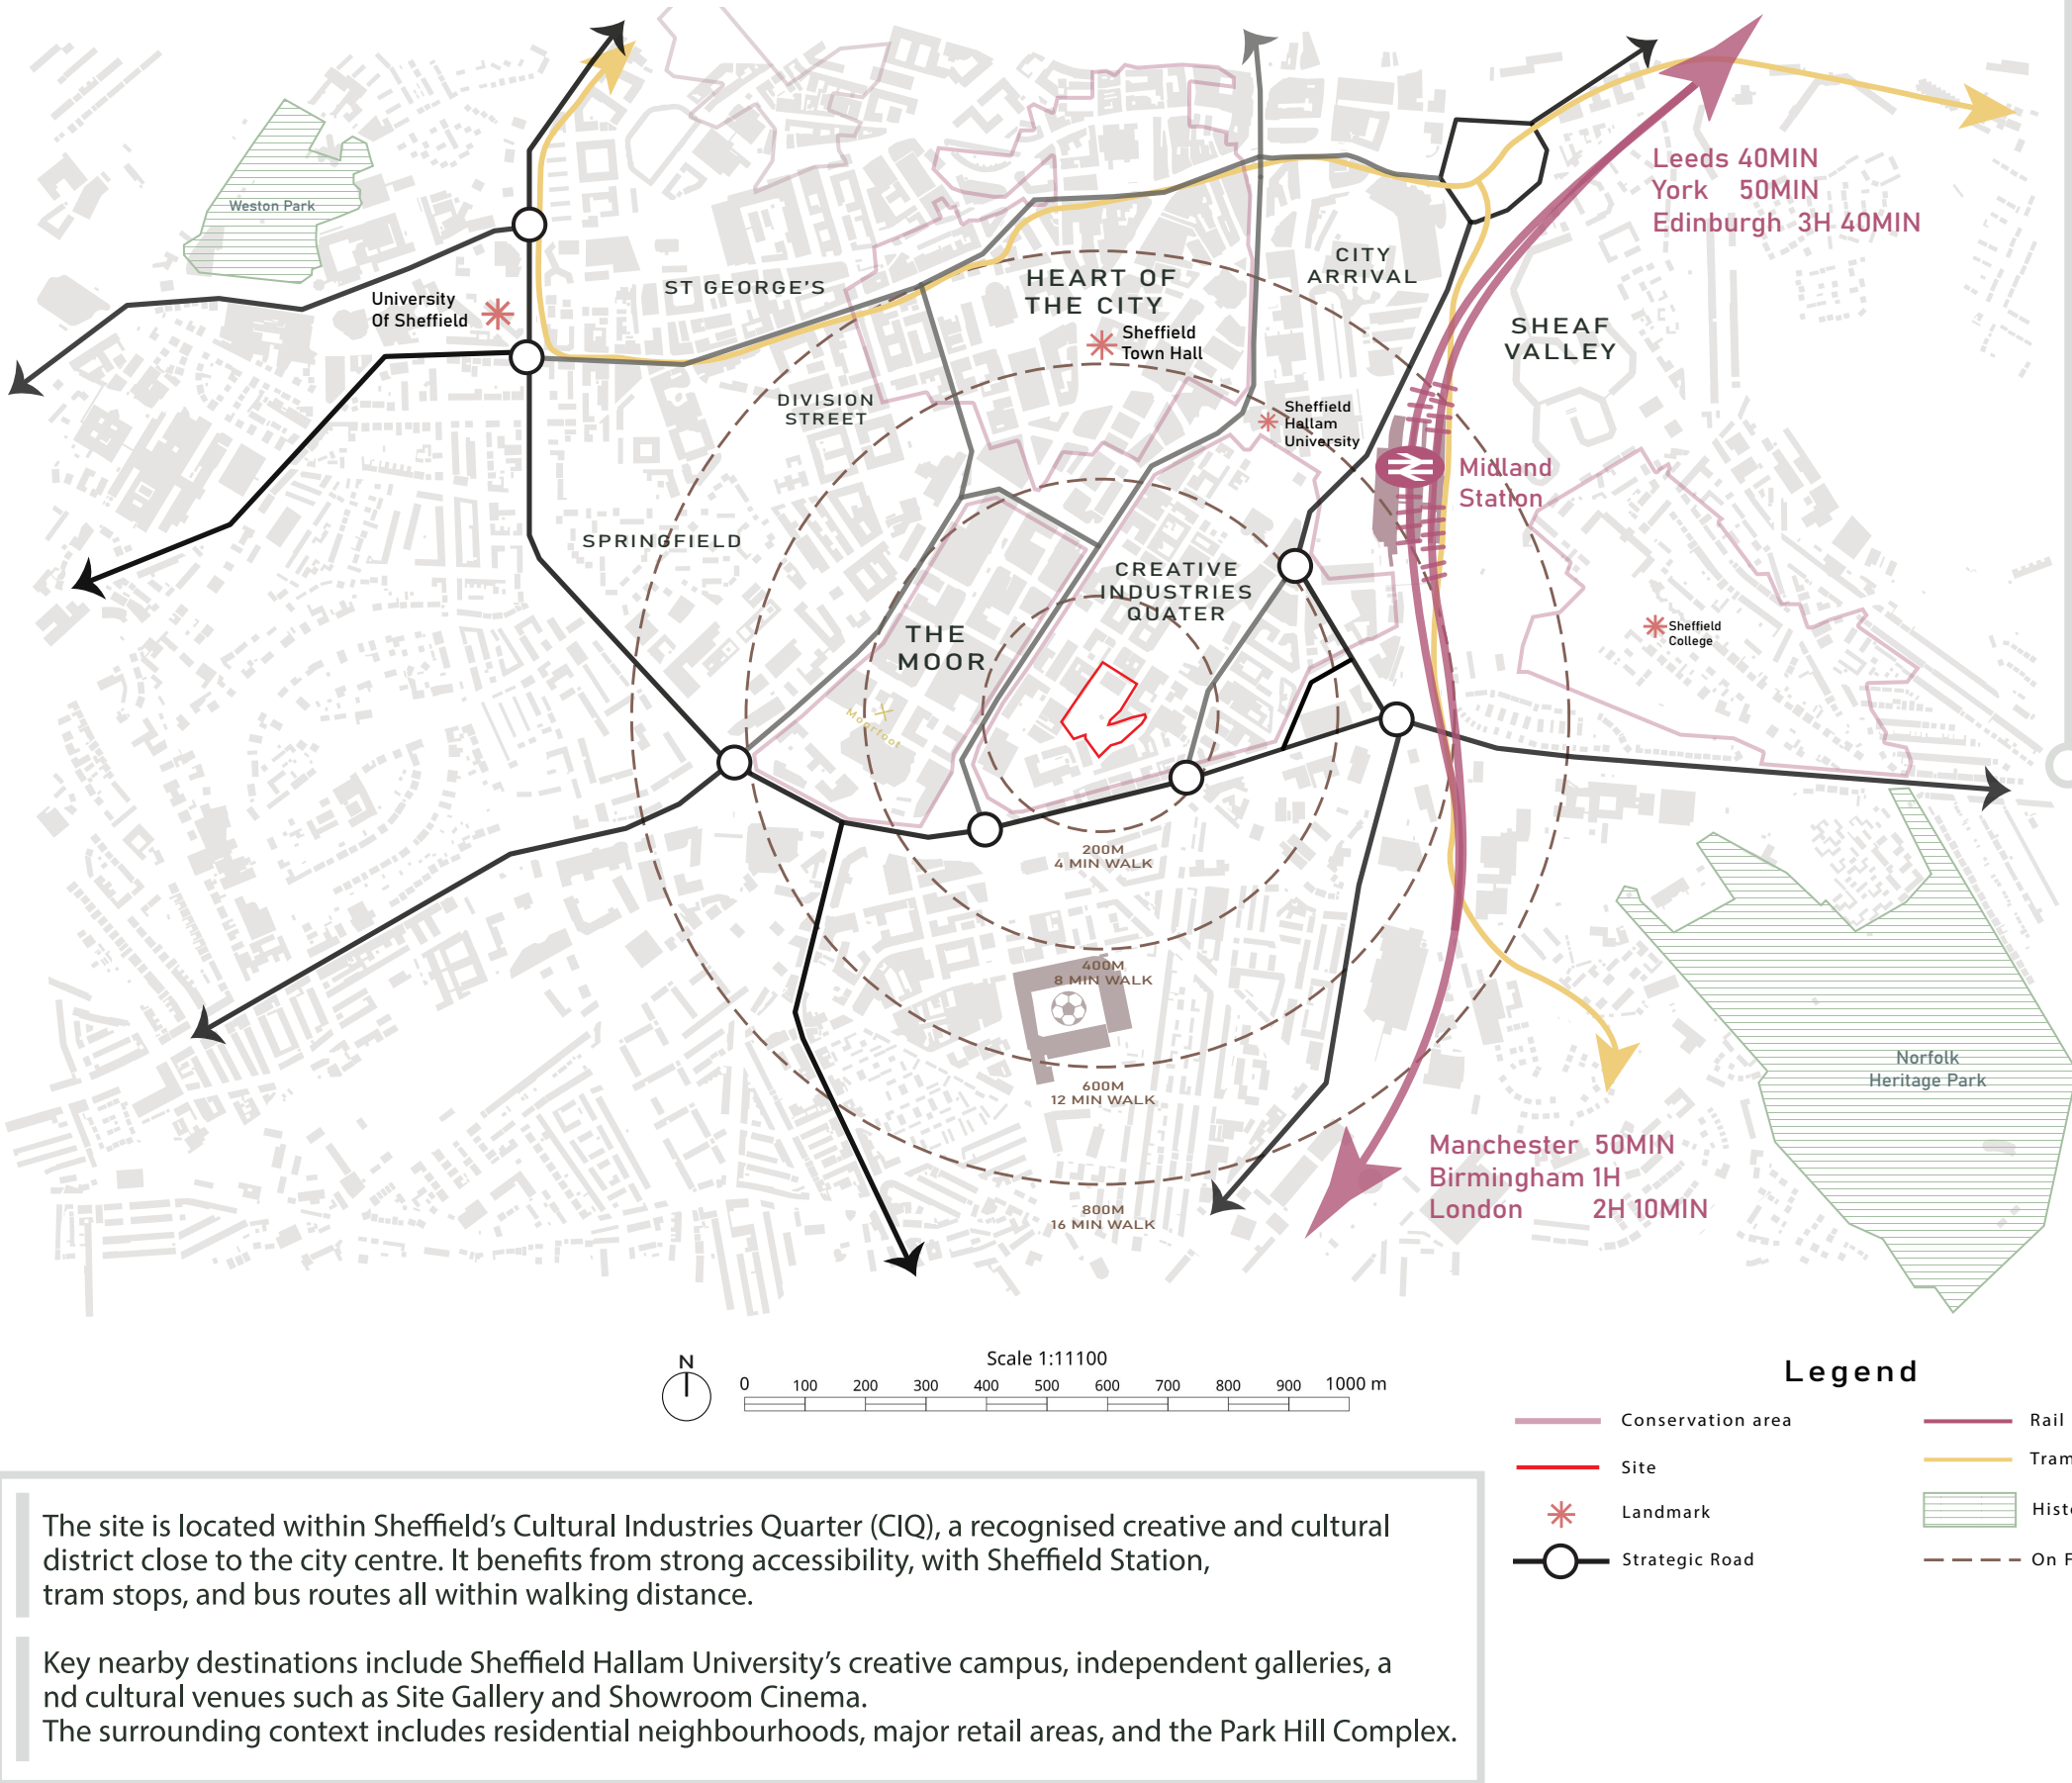

HISTORICAL ANALYSIS

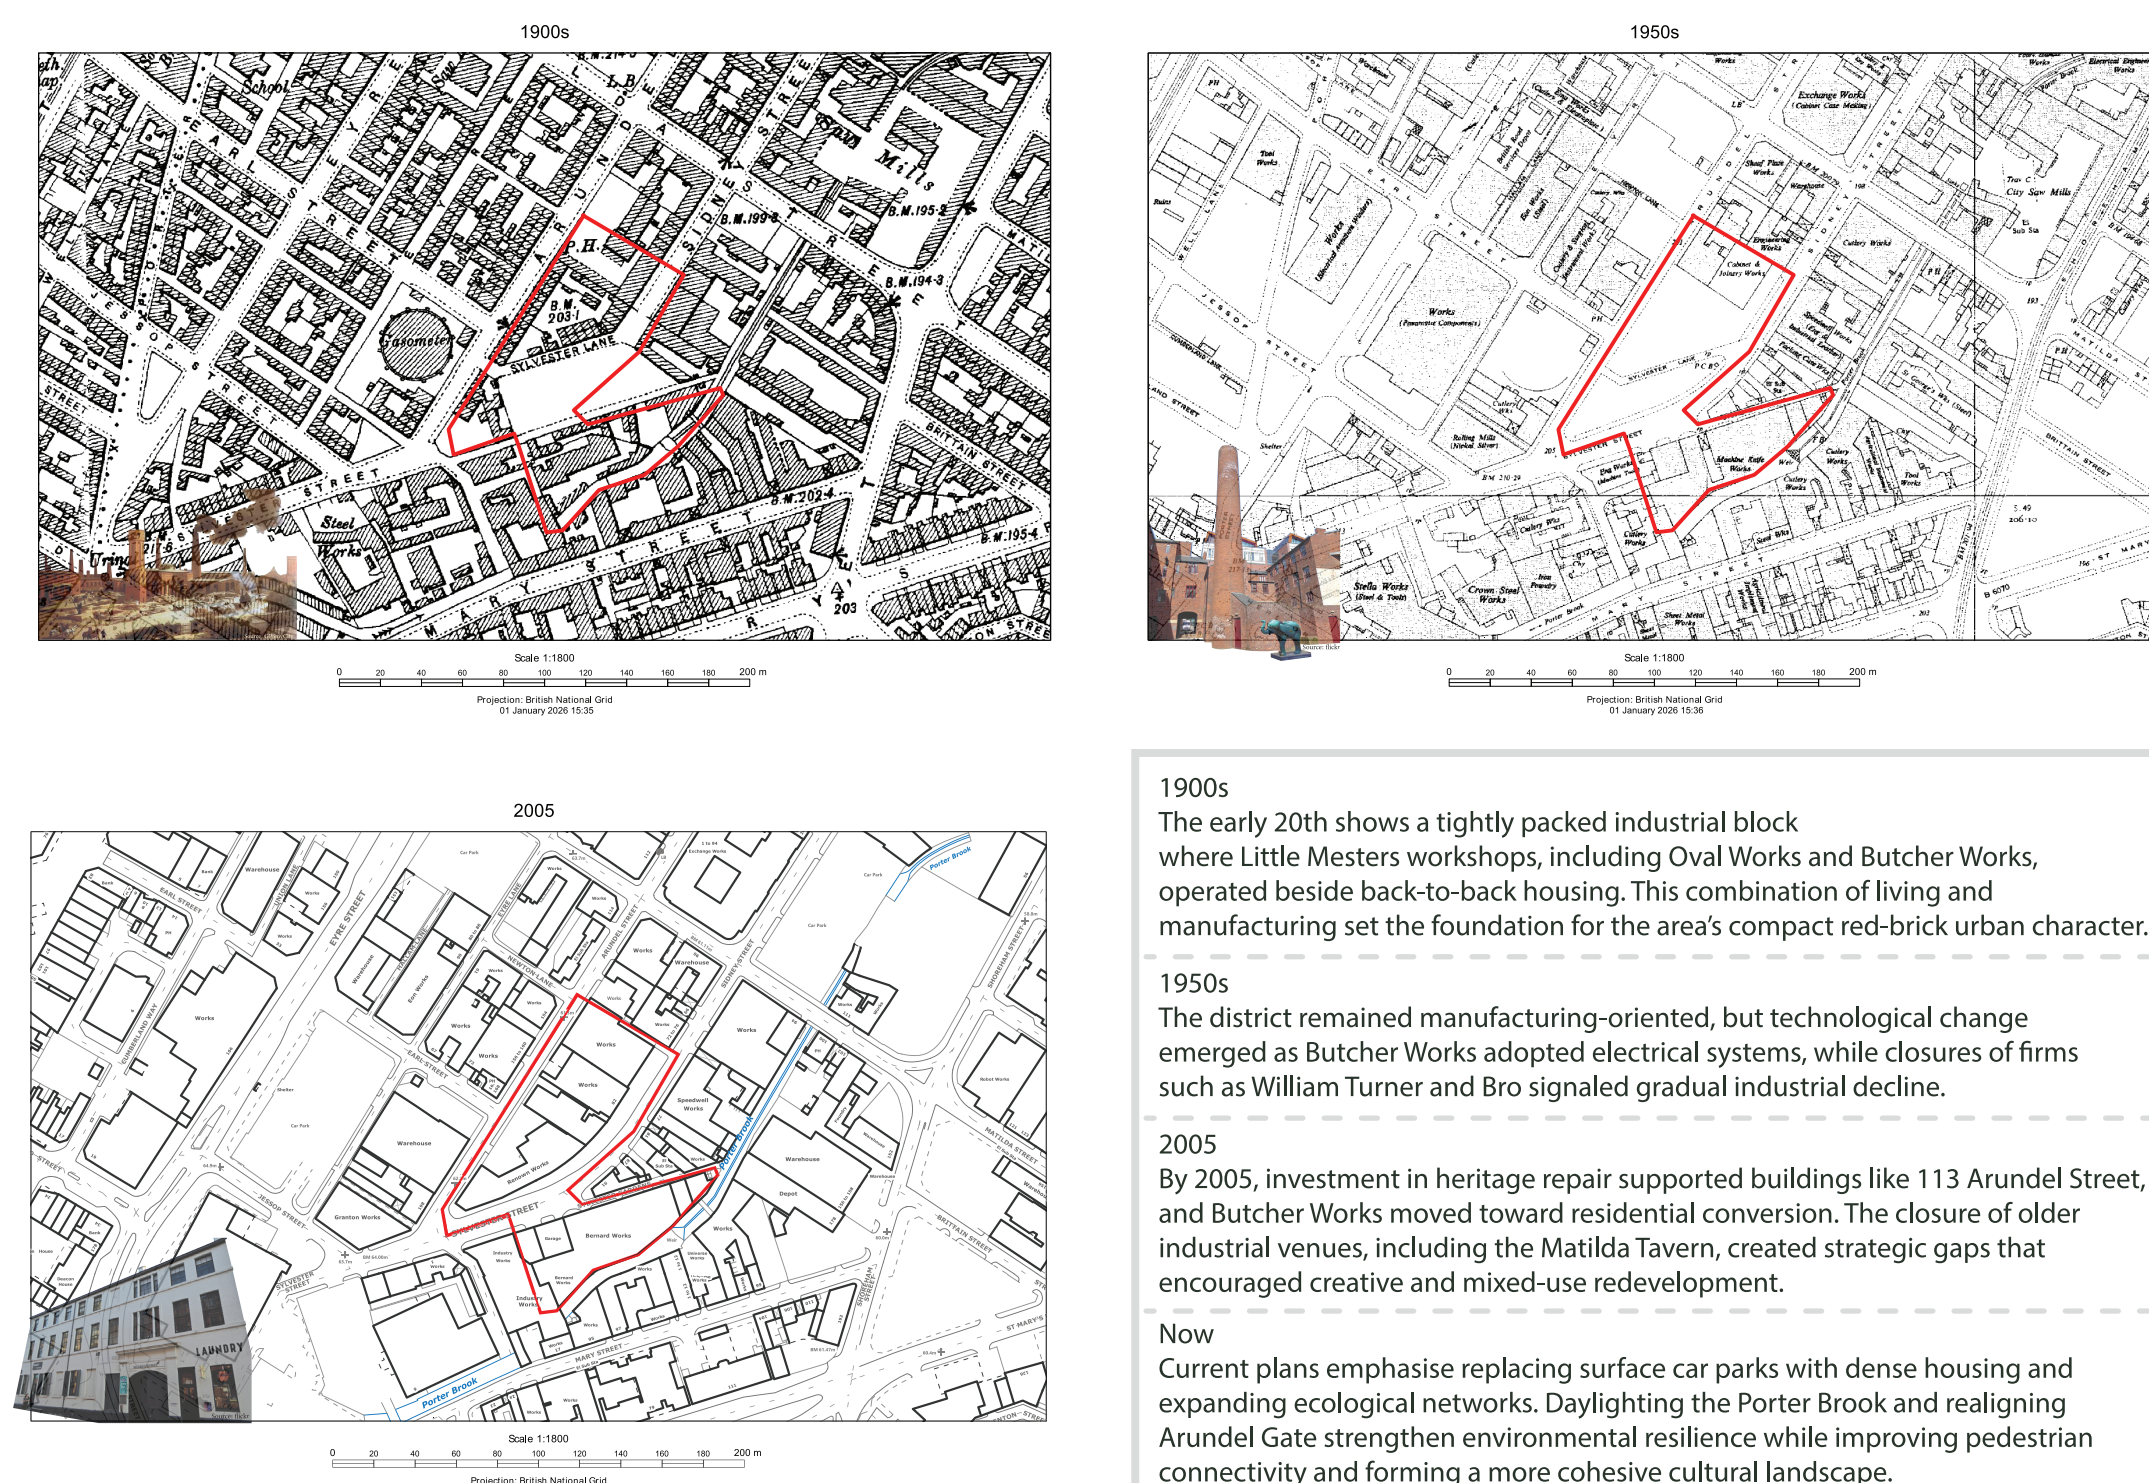


POLICY ANALYSIS

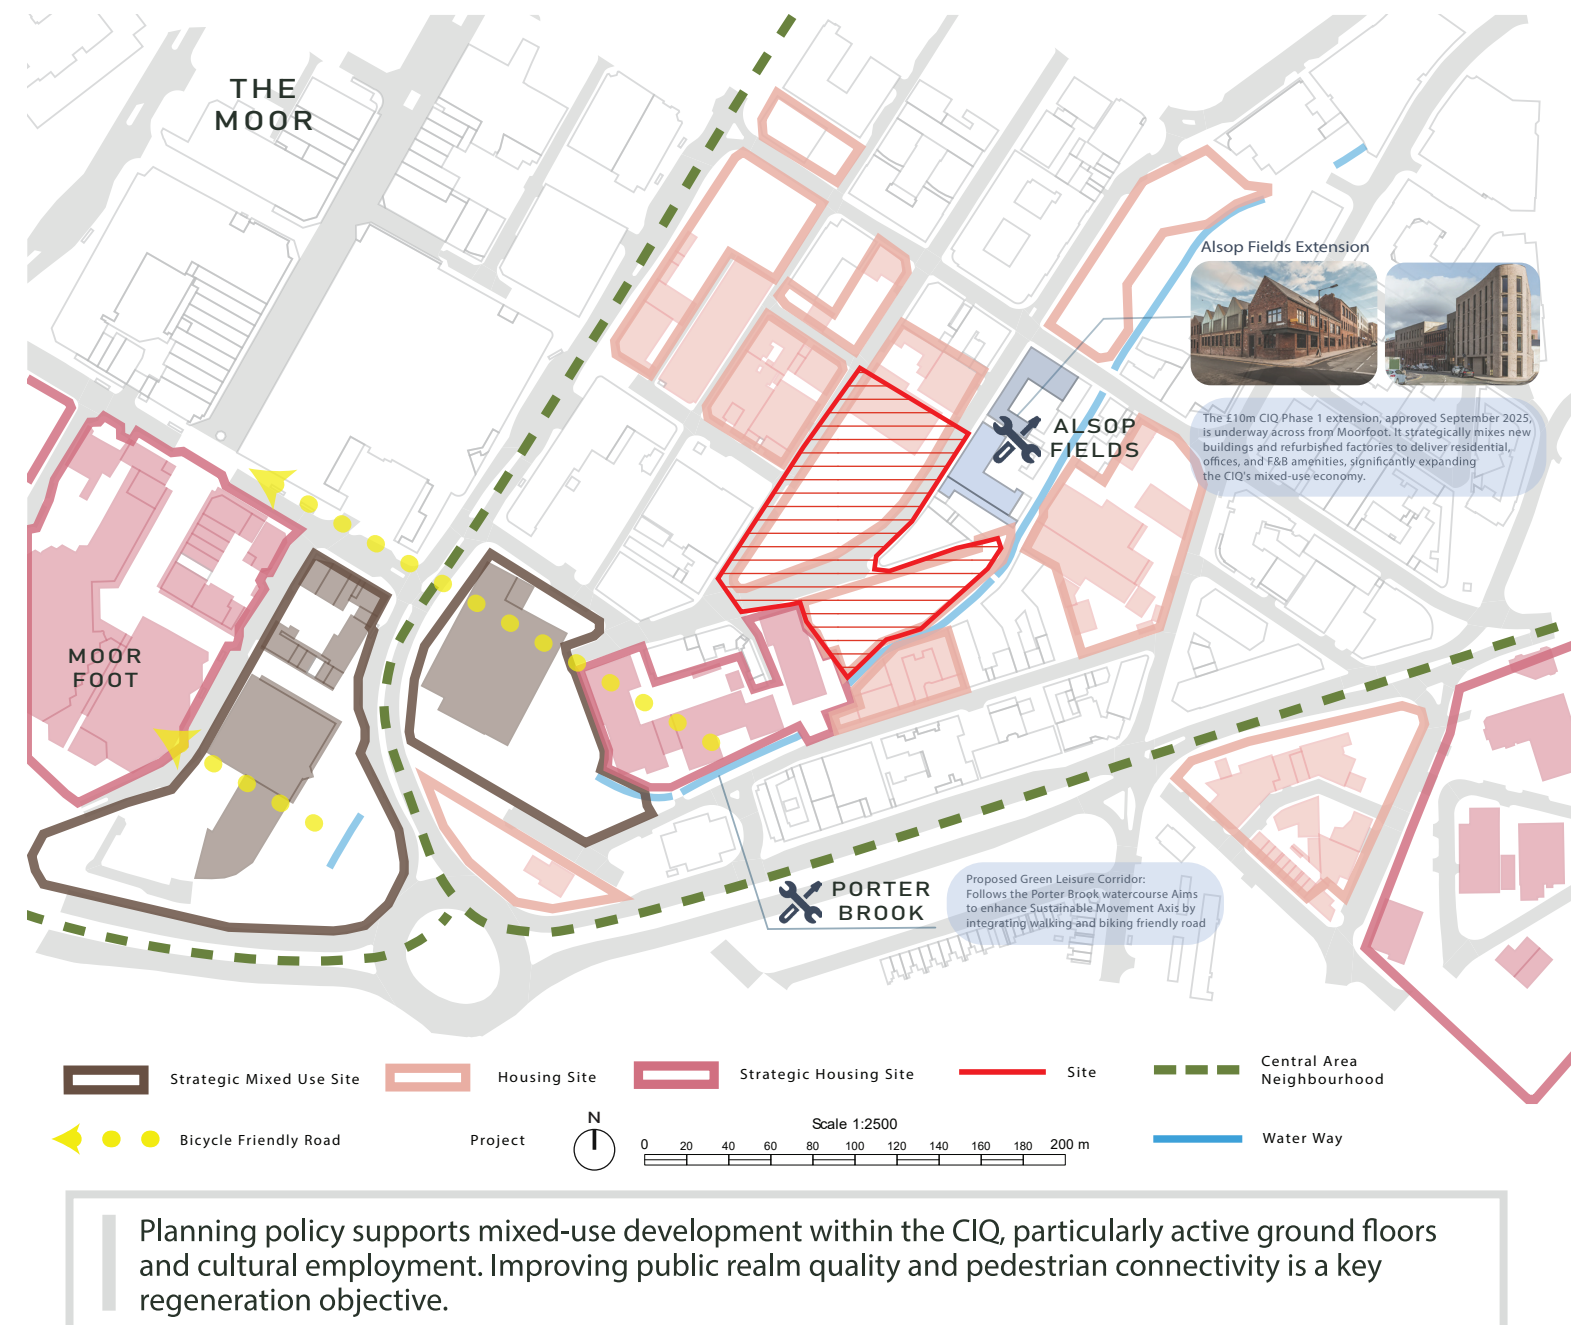

LAND USE



ROUTE HIERARCHY

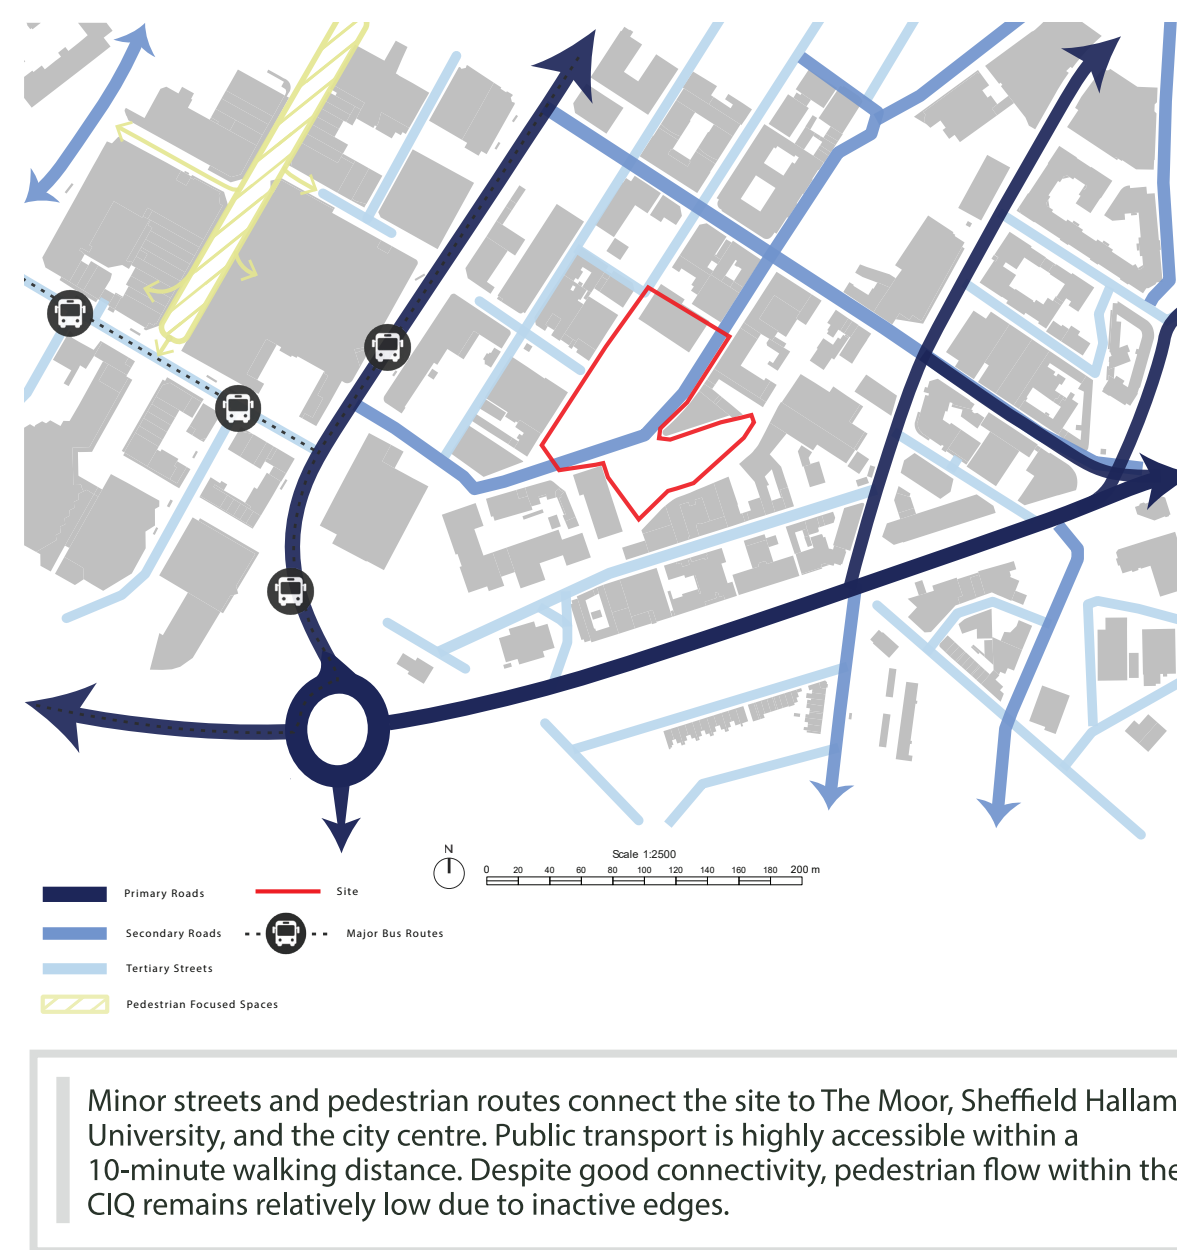

LEGIBILITY ANALYSIS



ACTIVE FRONTAGES & ACTIVITIES



DESIGN CONSIDERATIONS

OPPORTUNITIES

- Connectivity & Accessibility**
Low land efficiency seen in car parks located along the river, and vacant residential buildings, presenting opportunities for new mixed-use or interactive developments
- Potential Social Connection**
Potential role of local artists, designers, creative institutions to connect peoples
- Rich Historical Heritage**
Strong historical background, high value of listed buildings enhances CIQ's identity
- Potential Vibrant Pedestrian Corridor**
Several different activities in Arundel St, which can be used as a pedestrian path
- Potential Land for Development**
Low land efficiency seen in car parks located along the river, and vacant residential buildings, presenting opportunities for new mixed-use or interactive developments
- Porter Brook**
High-quality blue-green infrastructure & providing attractive waterfront public spaces, nature recovery and leisure
- Alsop Field Project**
As part of Alsop Fields, using bronze cladding and red brick creates a distinctive signature, enhancing the area's industrial streetscape

CONSTRAINTS



- Conservation Area**
being a conservation area that imposes strict controls on demolition limits flexibility of redevelopment
- High Proportion of Irrelevant Land Use**
Predominantly residential land-use in some areas reduces land-use efficiency and weakens the CIQs identity
- Limited Open Spaces**
Limited green and open public spaces, reducing opportunities for social interaction
- Lacking Significant Landmarks**
making navigation within the CIQ difficult
- Poor Condition Buildings**
Signs of physical disorder such as poor street conditions, neglected buildings, and urban decay contribute to insecurity

CIQ GATEWAY DESIGN PROPOSAL


DESIGN OPTION 1 || DESIGN OPTION 2

FINAL DESIGN OPTION


DESIGN BRIEF

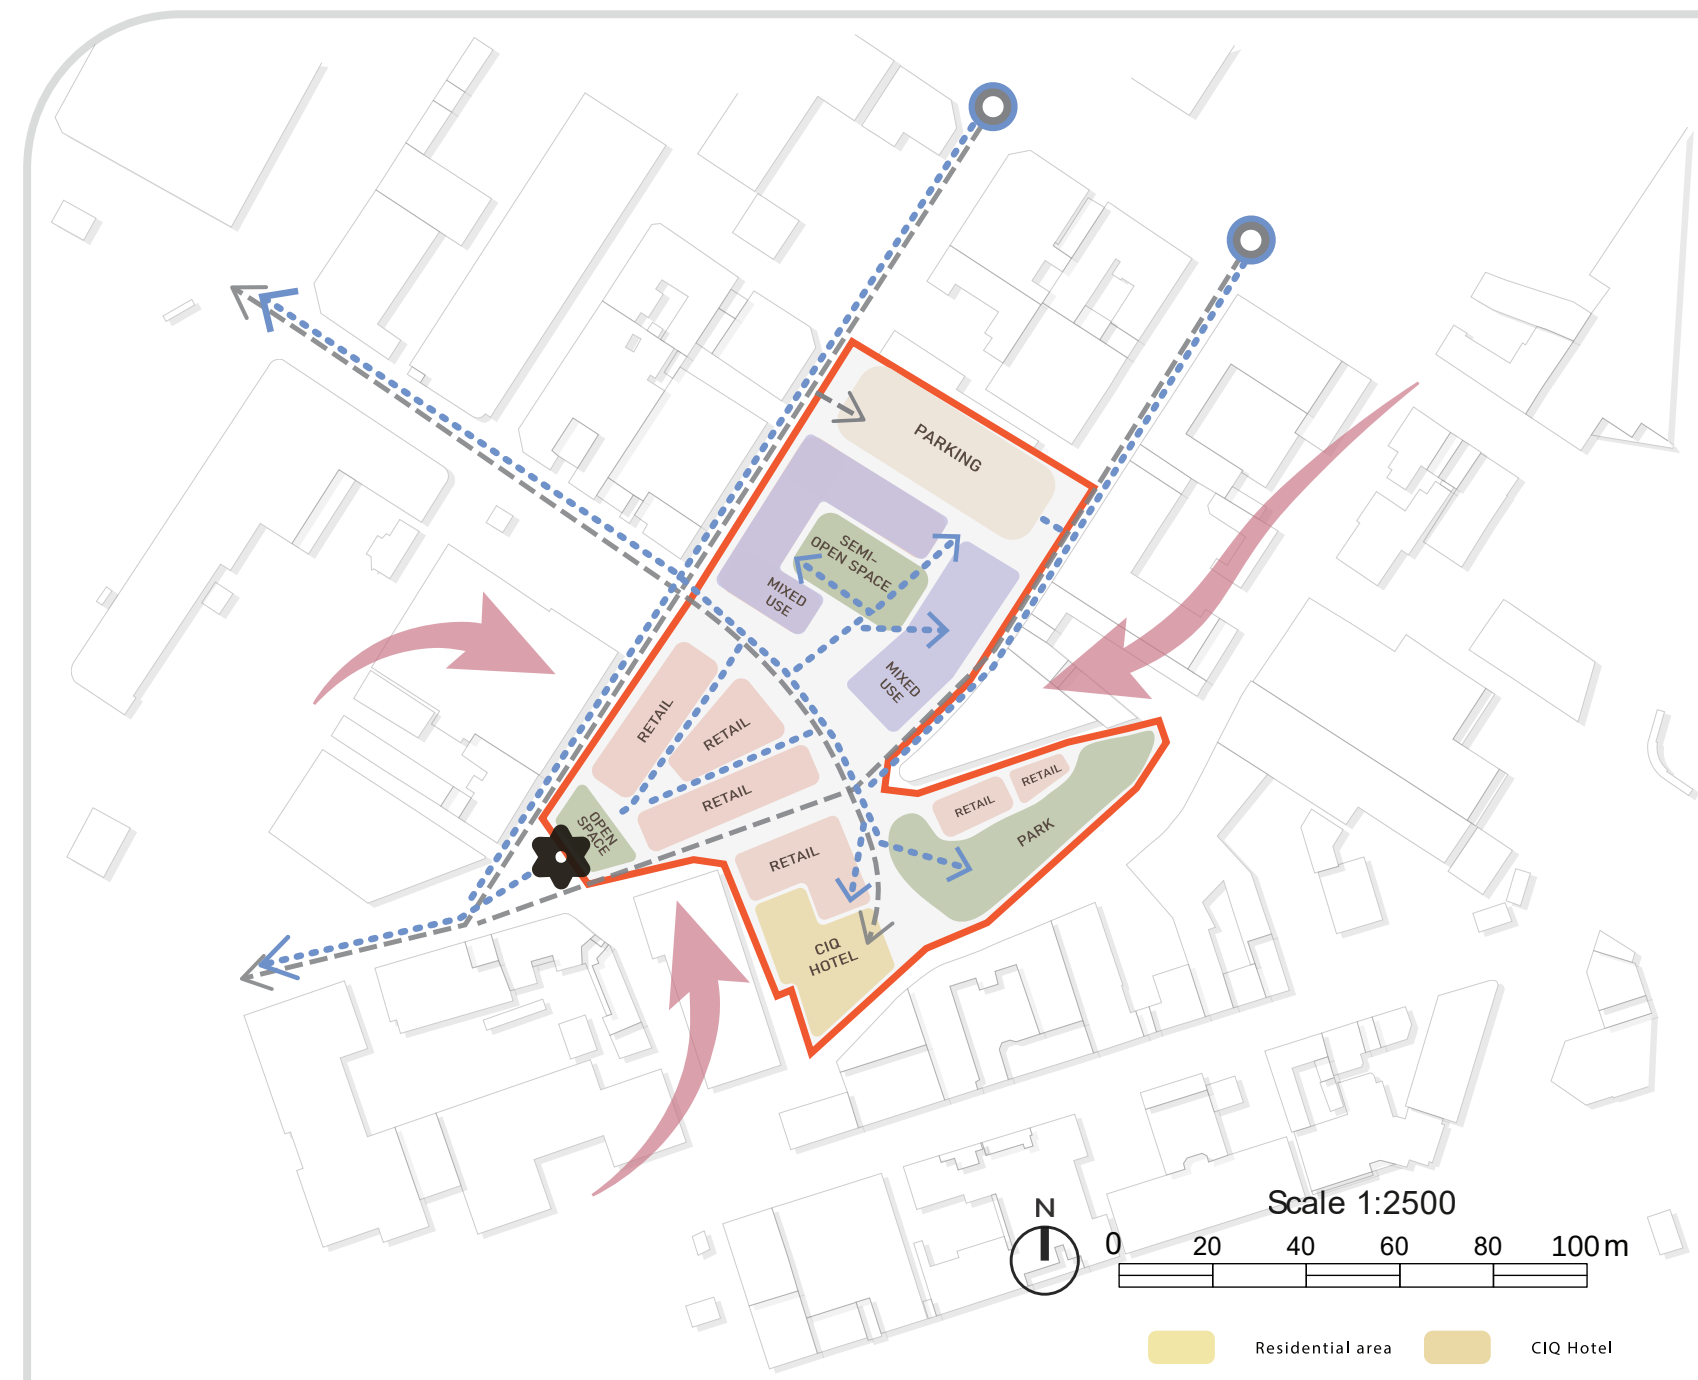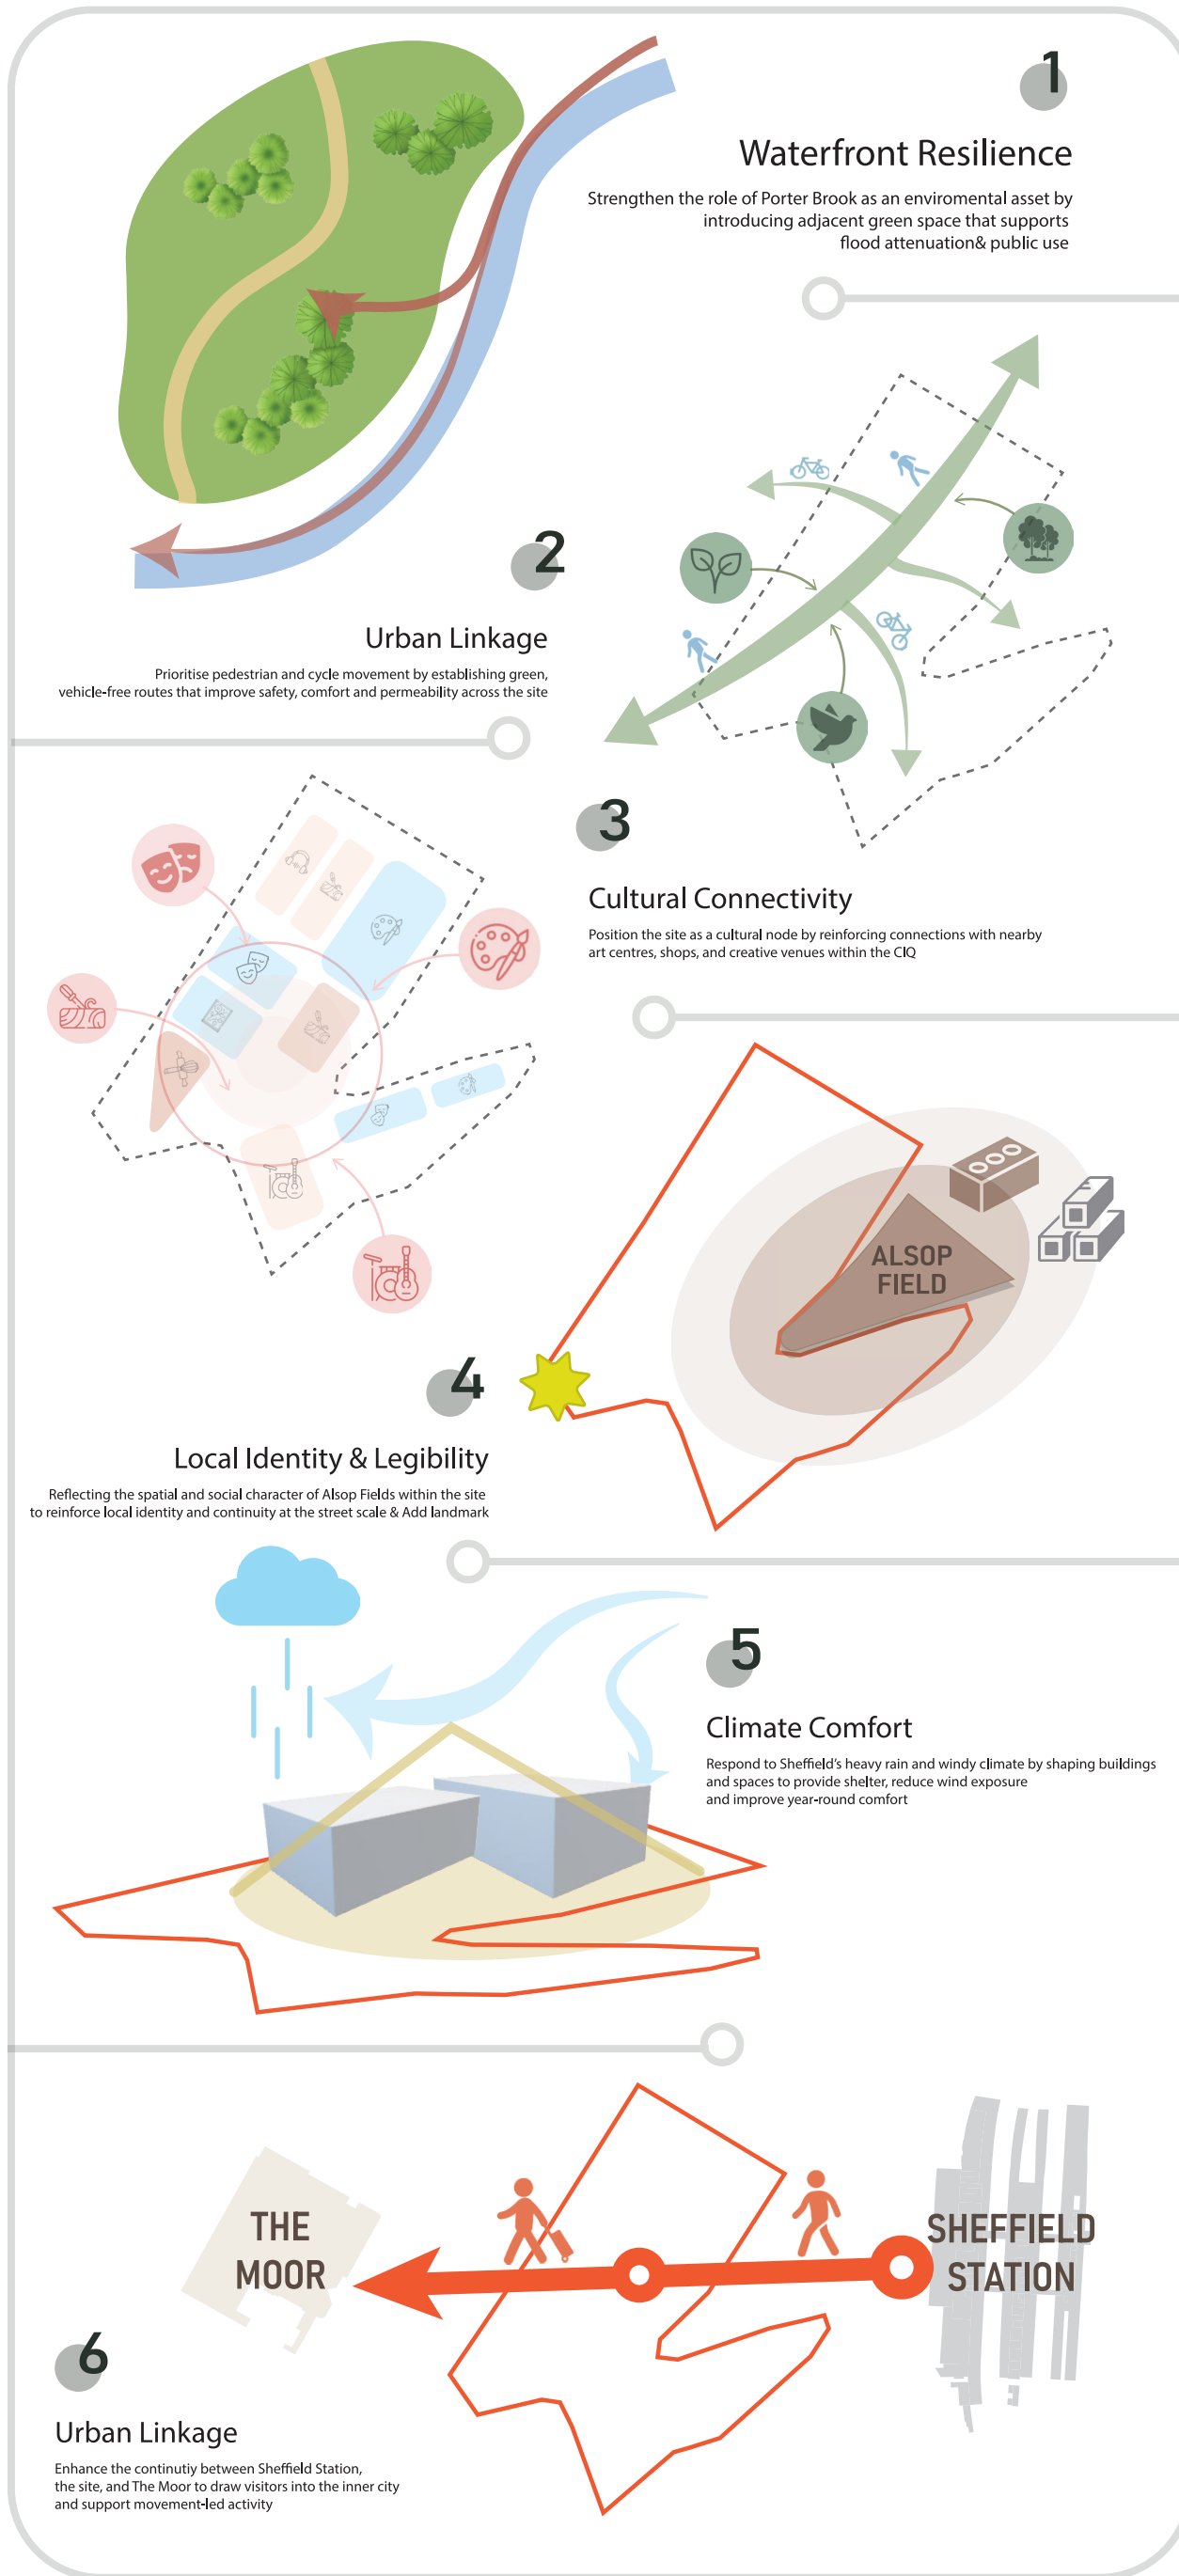

This option focuses on a pedestrian focused retail street that draws visitors into the site, anchored by a landmark open space. U-shaped mixed-use office blocks provide shelter from Sheffield's wind and rain, while a large park, entertainment-led retail, and a CIQ hotel activate the flood resilient Porter Brook edge.

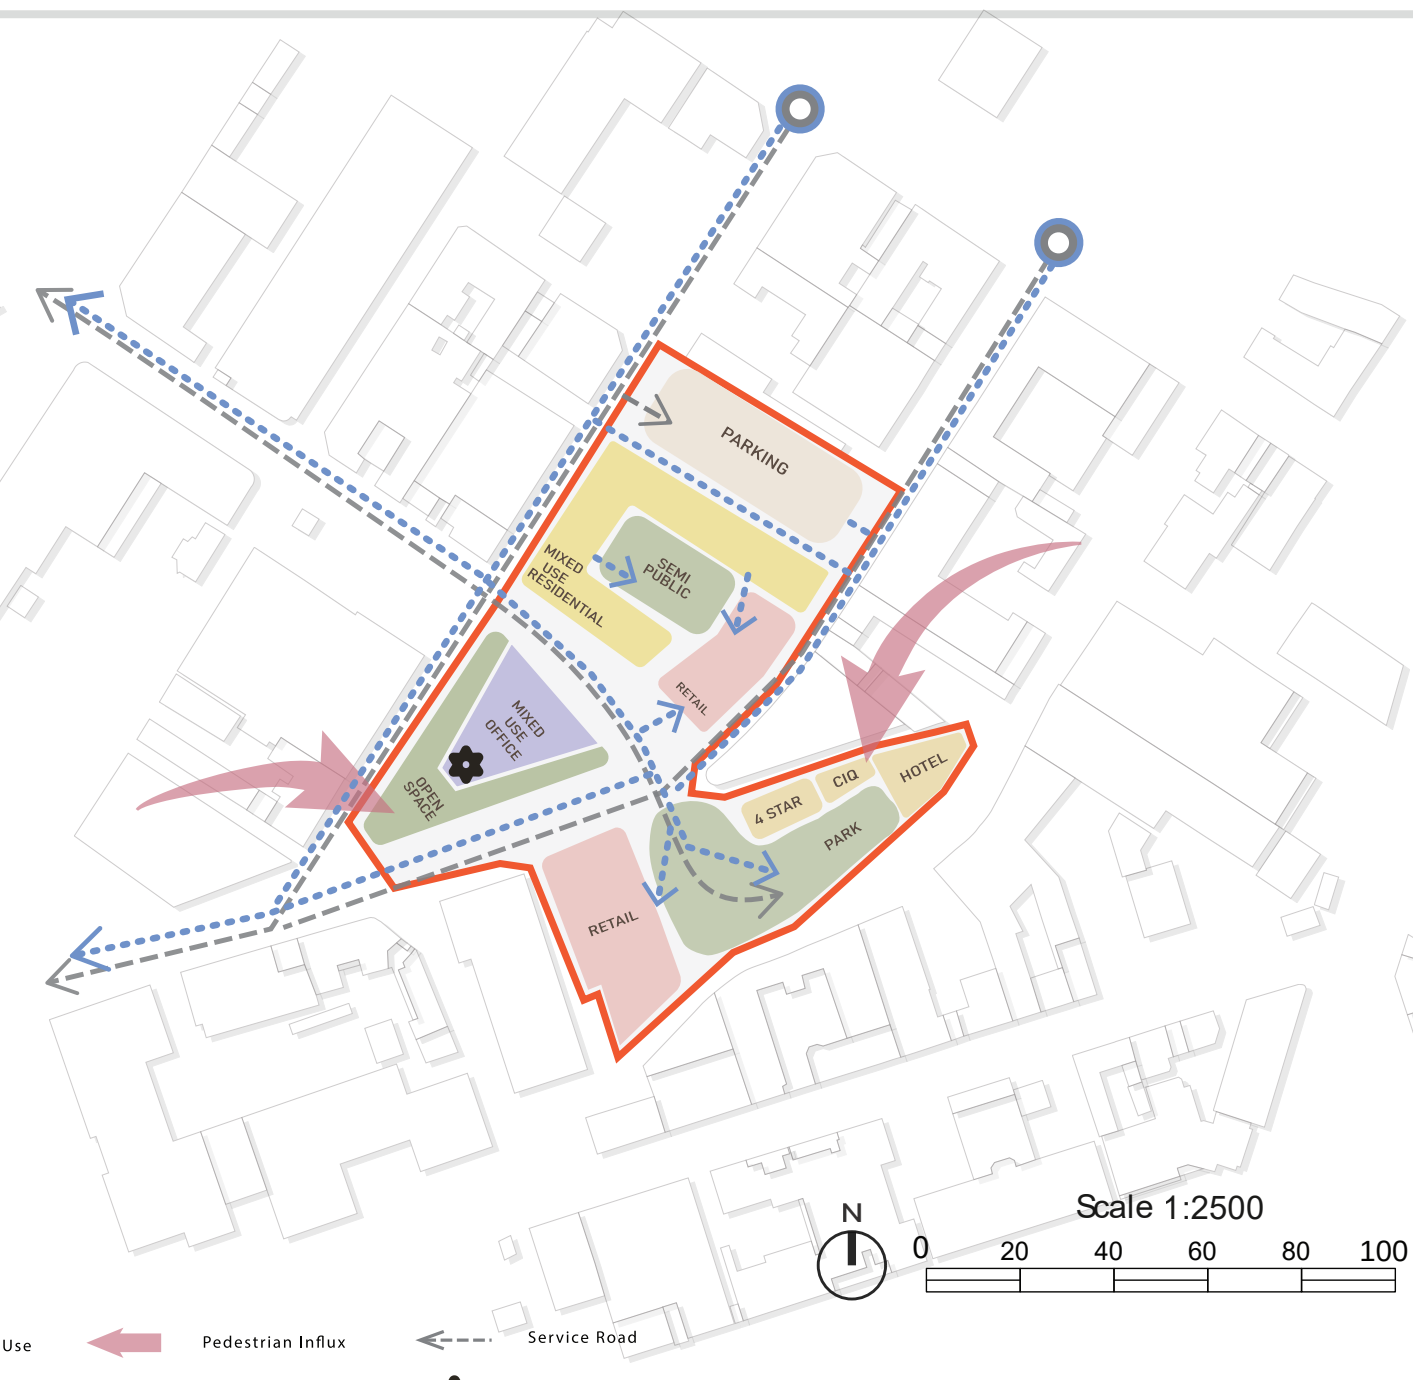


This option replaces the open-space landmark with a mixed-use office fronting a public open space, establishing a built landmark. Residential blocks support daily activity, while a 4 star CIQ hotel and retail along the park edge attract visitors and strengthen the site's destination character.

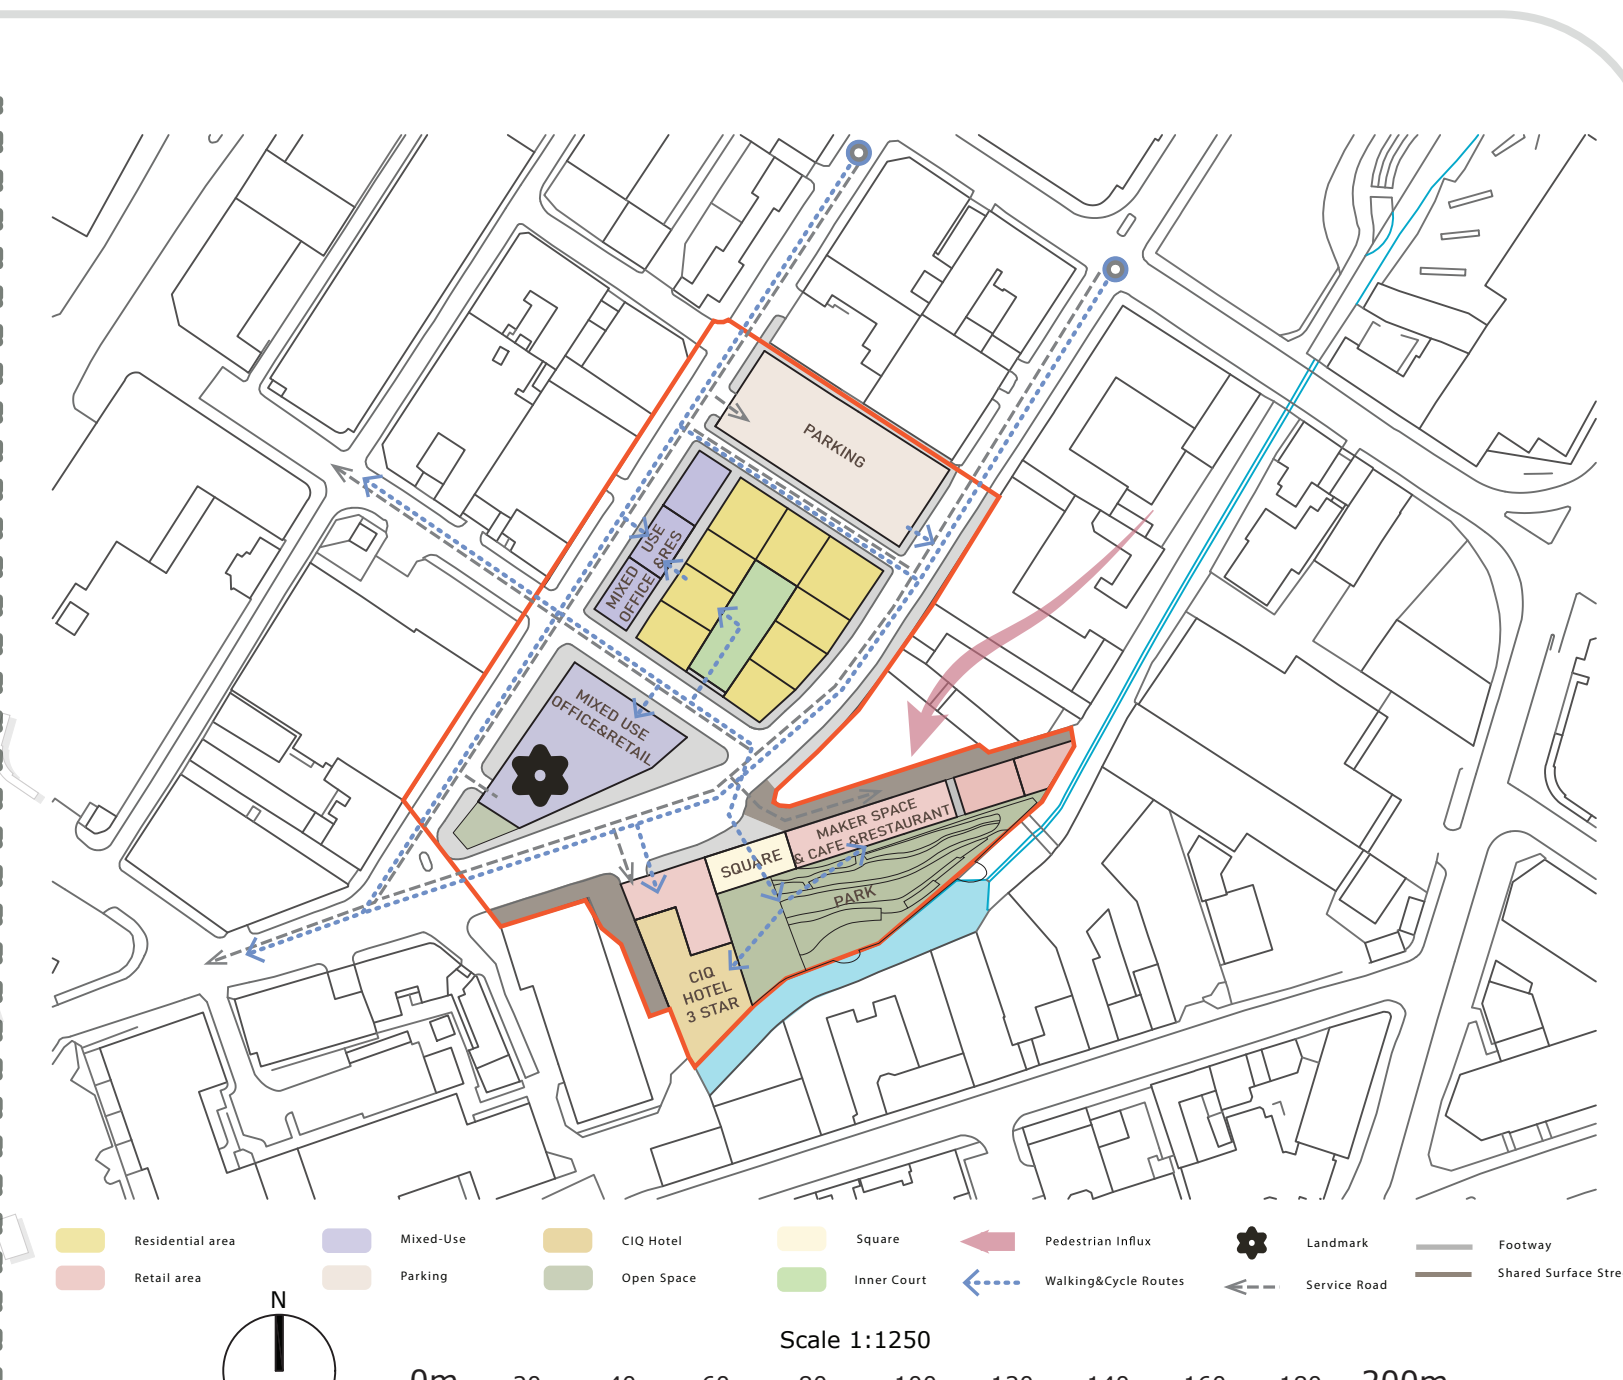

The final design integrates the CIQ Hotel and park from Option 1 with the mixed-use office, residential spaces, and parking building from Option 2. This layout aims to maximize the site's spatial value while effectively fulfilling our client requirements and urban goals.

FINAL DESIGN PROPOSAL

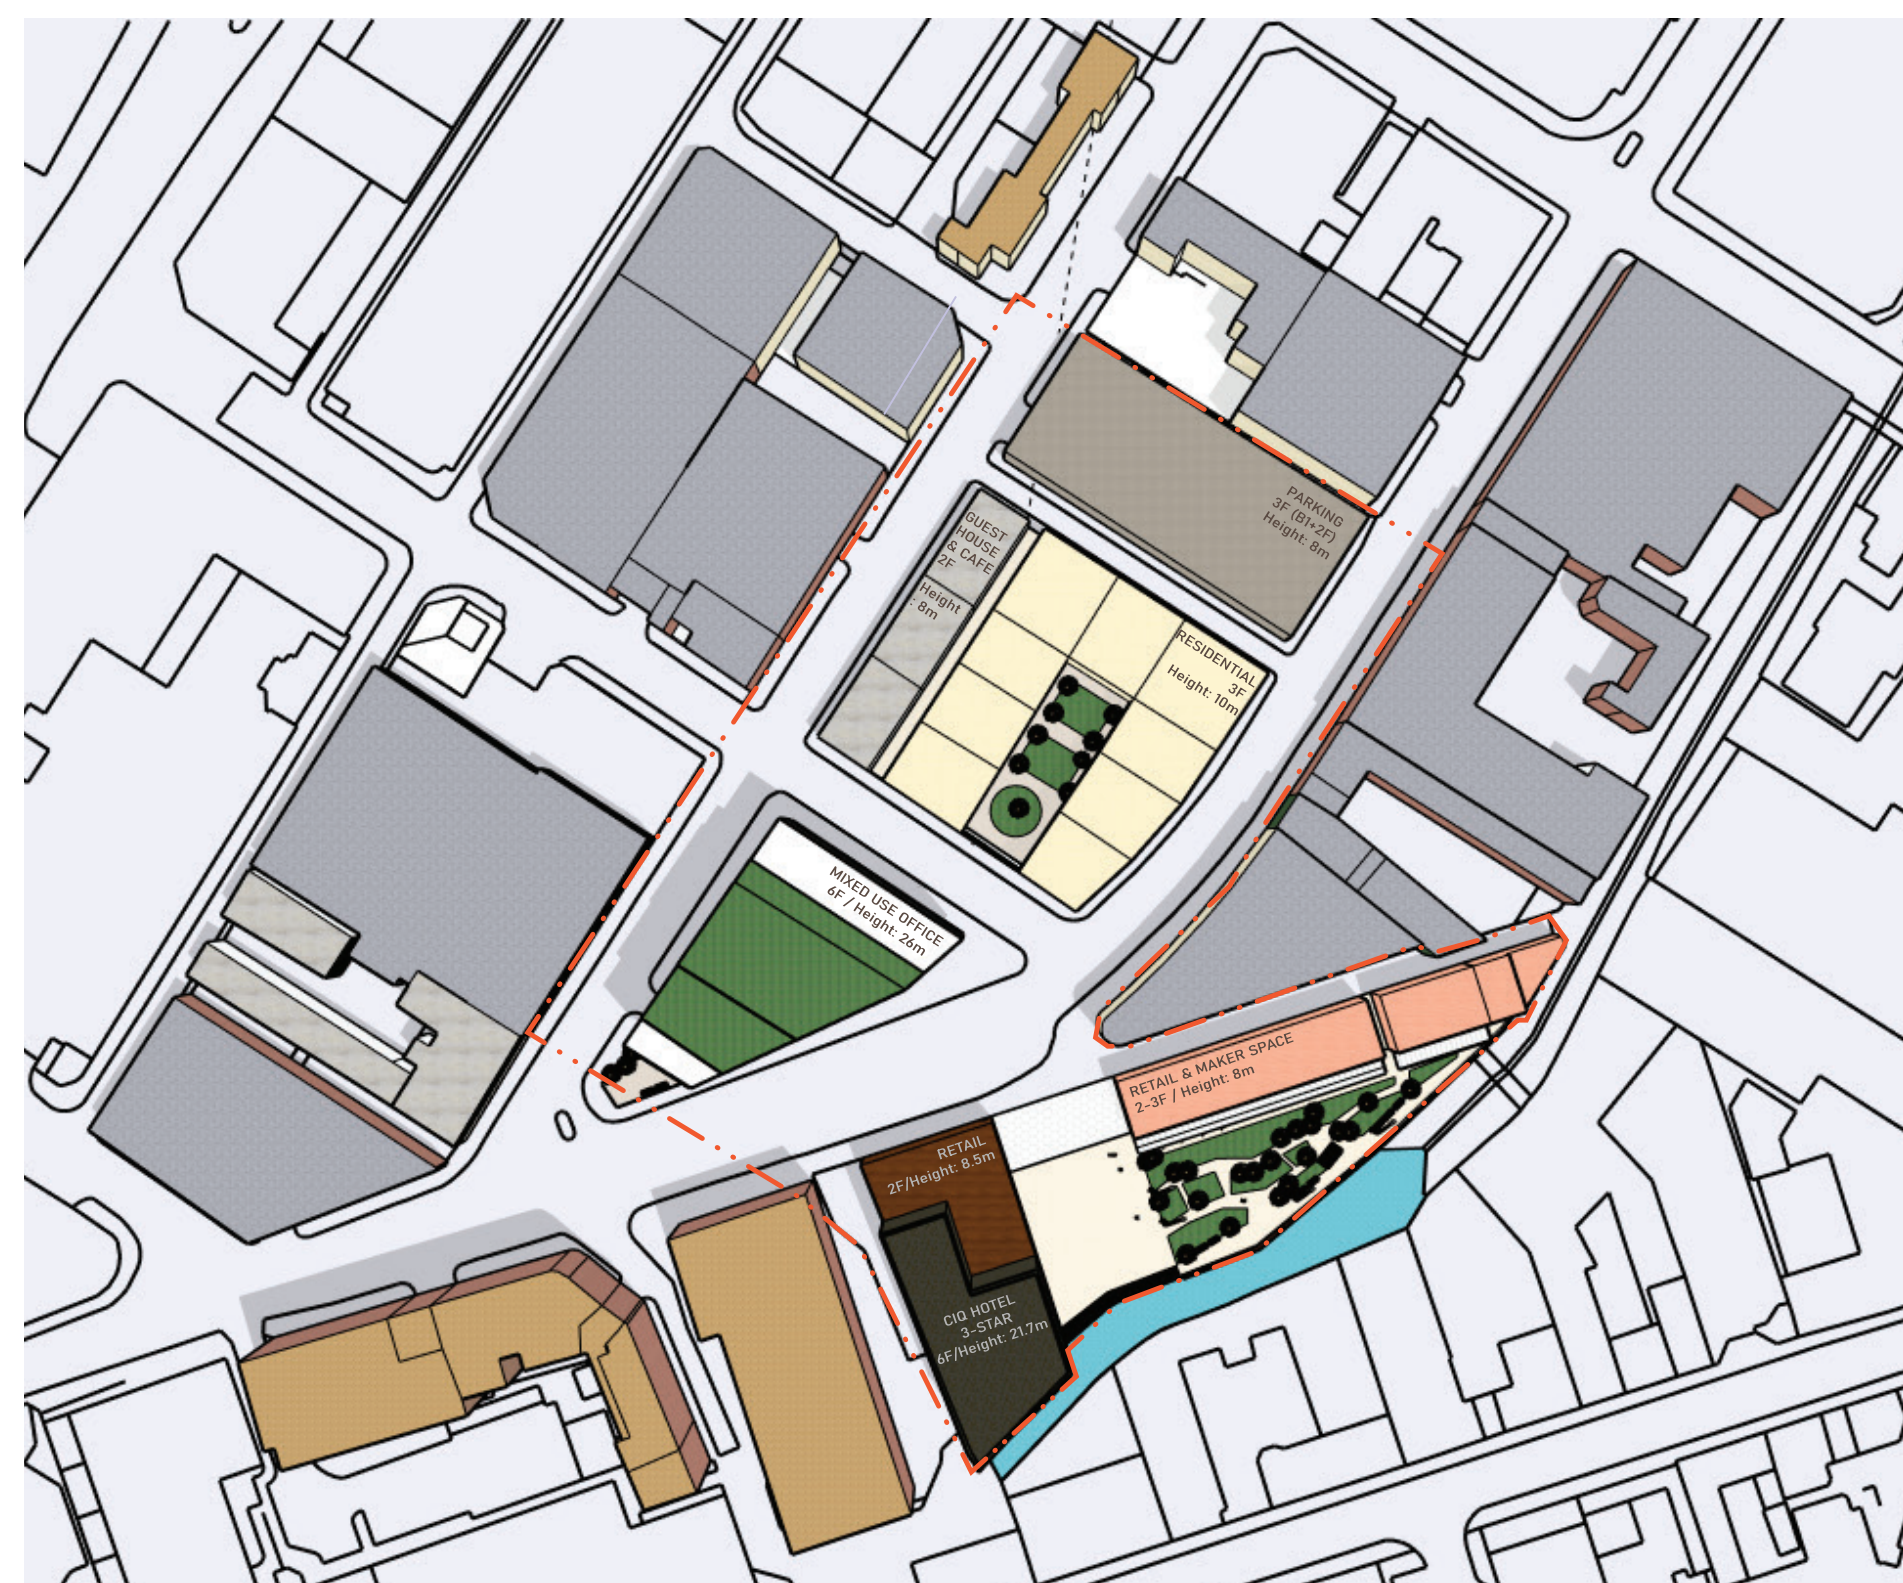

MIXED USE OFFICE



Features a public lobby/cafe 1F, Office Units A & B (2 floors per unit) 2-5F, and a rooftop sky lounge with shared meeting spaces 6F. A setback roof protects residential views, while contrasting cladding creates a distinctive landmark.

RESIDENTIAL



The residential section adopts a U-shaped layout for wind protection, with a central courtyard ensuring privacy. The exterior features light-coloured brick cladding.

CIQ HOTEL



Comprises a podium 1F: Lobby, Retail, Gallery 2F: Restaurant/Bar and lifestyle rooms 3-6F. The expanded podium maximizes street-level engagement.

PARK




Includes a terraced deck for busking, a flood-resistant boardwalk, and green spaces for relaxation + flexible zones for pop-up markets.


MOOR - MIXED USE OFFICE



TOP VIEW OF LANDMARK TO PARK

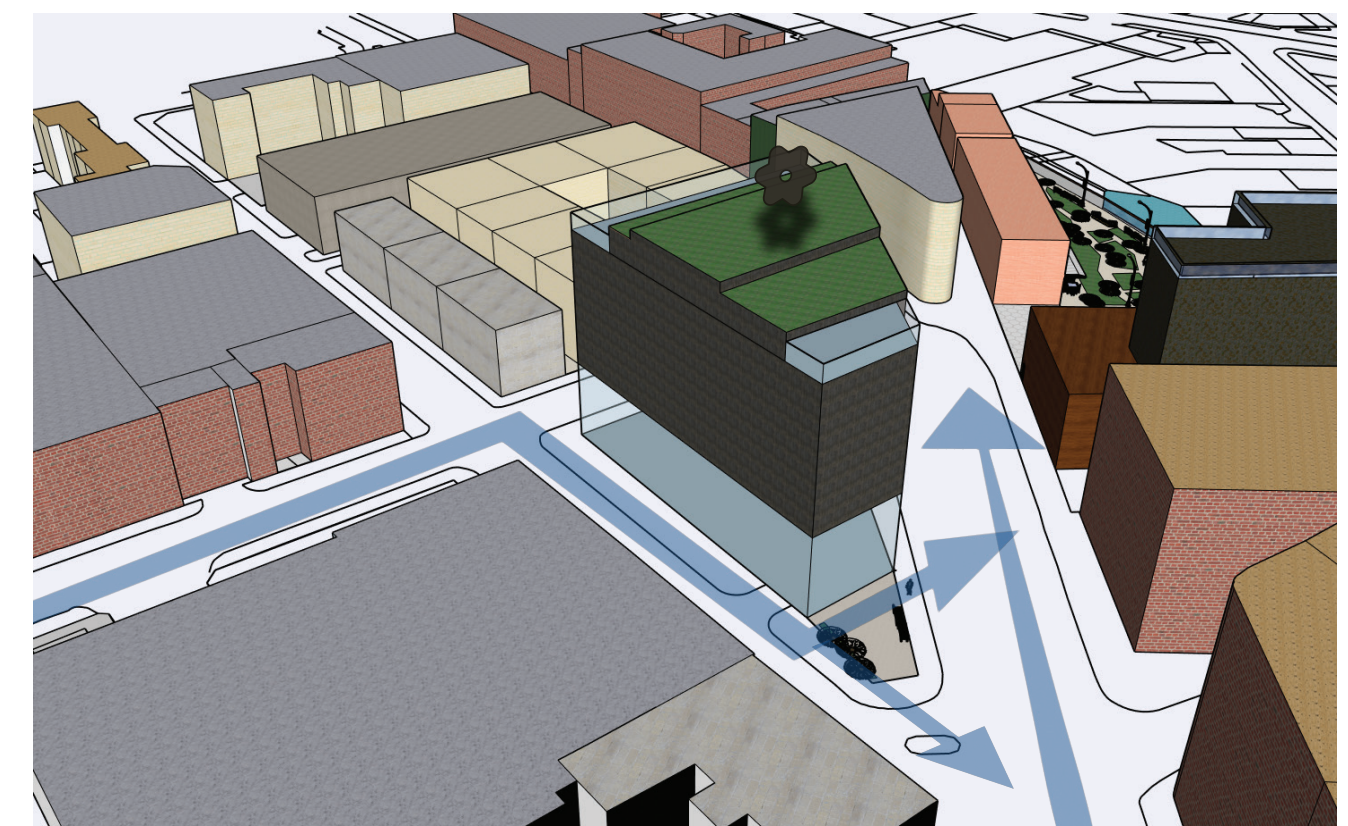

SIDE-TOP VIEW (SETTING: JAN 25 10AM)

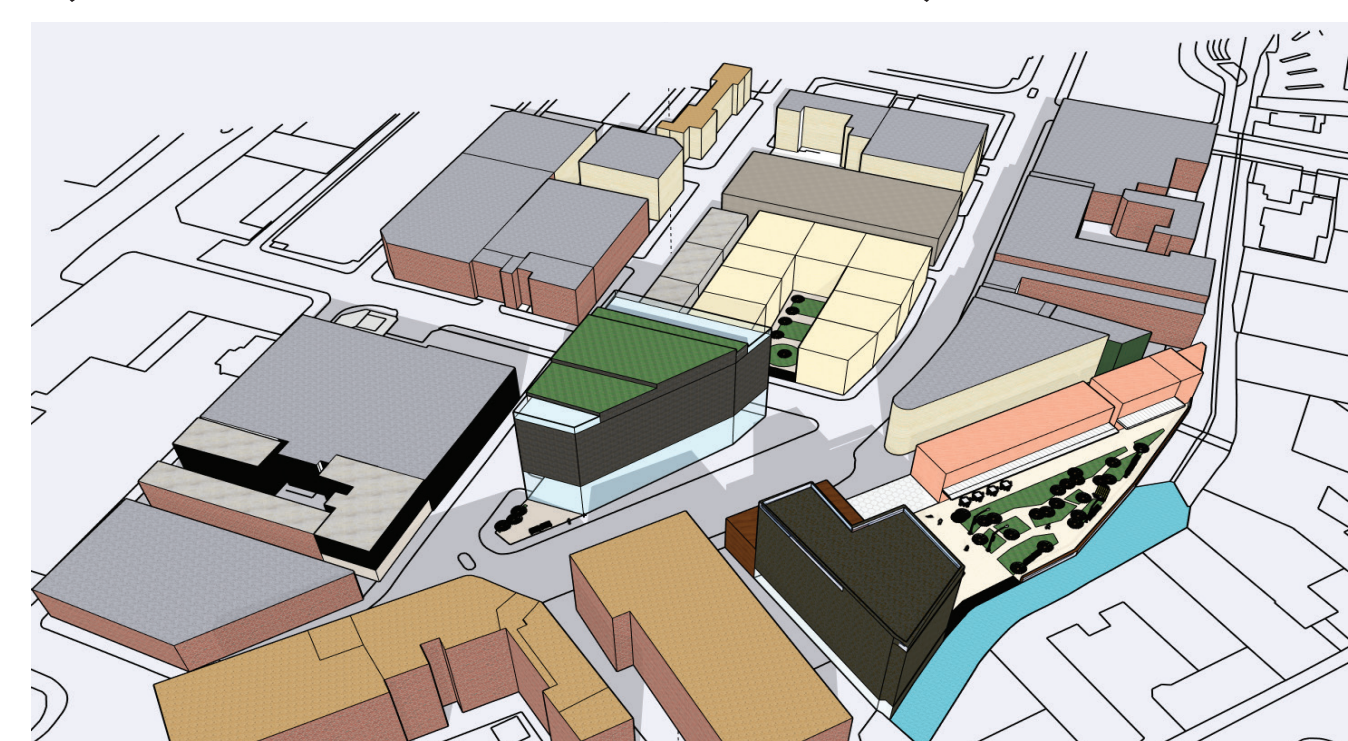


MEASUREMENT



REVITALISING SHEFFIELD'S CIQ

This design focuses on transforming the site into a central CIQ hub by celebrating Sheffield's cultural identity. By integrating entertainment elements into the eco-park and prioritizing pedestrian-friendly, sustainable live communities, the site becomes a landmark that respects local heritage.

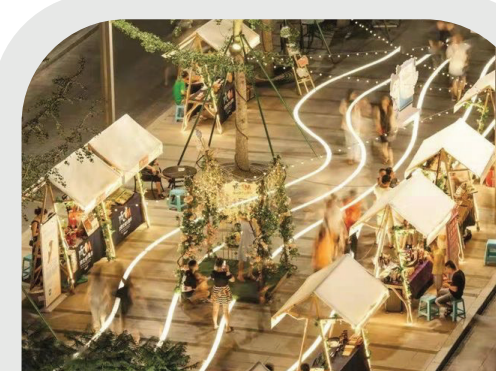

Maker spaces, craft shop, and cafes line the pedestrian pathways to foster a vibrant maker culture.

RETAIL & MAKER SPACE



Contemporary use of Corten steel and red brick reflects Sheffield's industrial history through a modern architectural design.